

Kugathas Kugarajah

UK Architect (ARB / Part III)

Freelance
Remote Planning & Technical Support

Email: kkugarajah2@gmail.com
Phone: +44 7543 452019



PROFILE

UK architect with 10+ years' experience delivering residential and commercial projects across the UK. I provide remote support to architectural practices on planning applications, technical and construction drawing packages, and consultant coordination, integrating quickly into existing teams to add capacity where needed.

SERVICES OFFERED

Planning applications and amendments (including Section 73)

Technical / construction drawing packages (Stages 3–4)

Consultant coordination and drawings integration

All drawings, visuals and details shown produced by myself

(site photos taken by others)



WILDERNESSE RESTAURANT

For Morris + Company

**Delivery Architect
Stages 4 & 5**

Key Skills:

Producing GA drawings & construction details

Producing 3D diagrams and details


Site inspections

Coordinating contractor information


Quality control

Product specification

NBS Specification






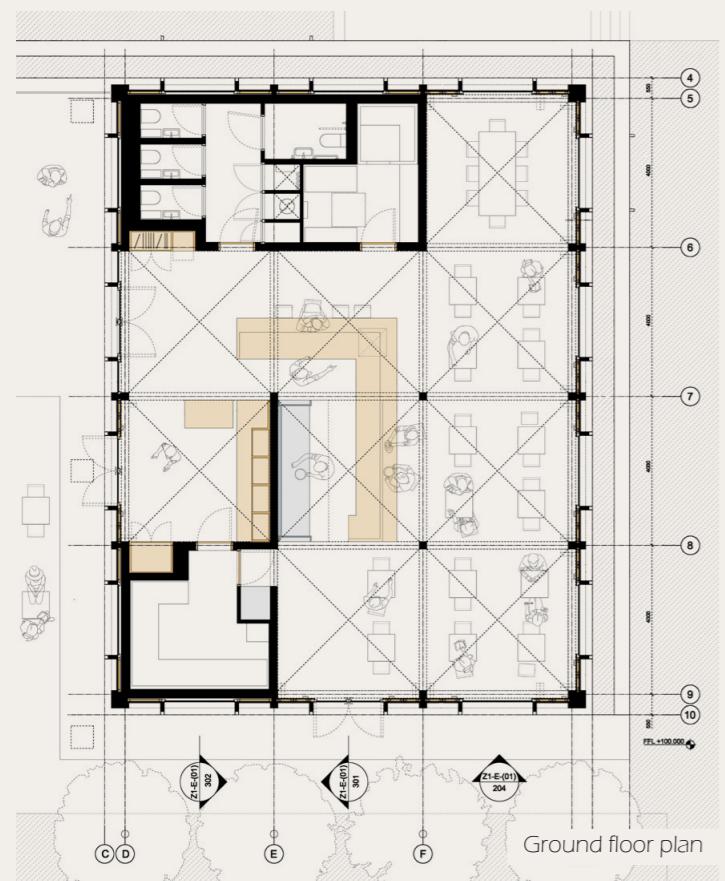


Physical models production


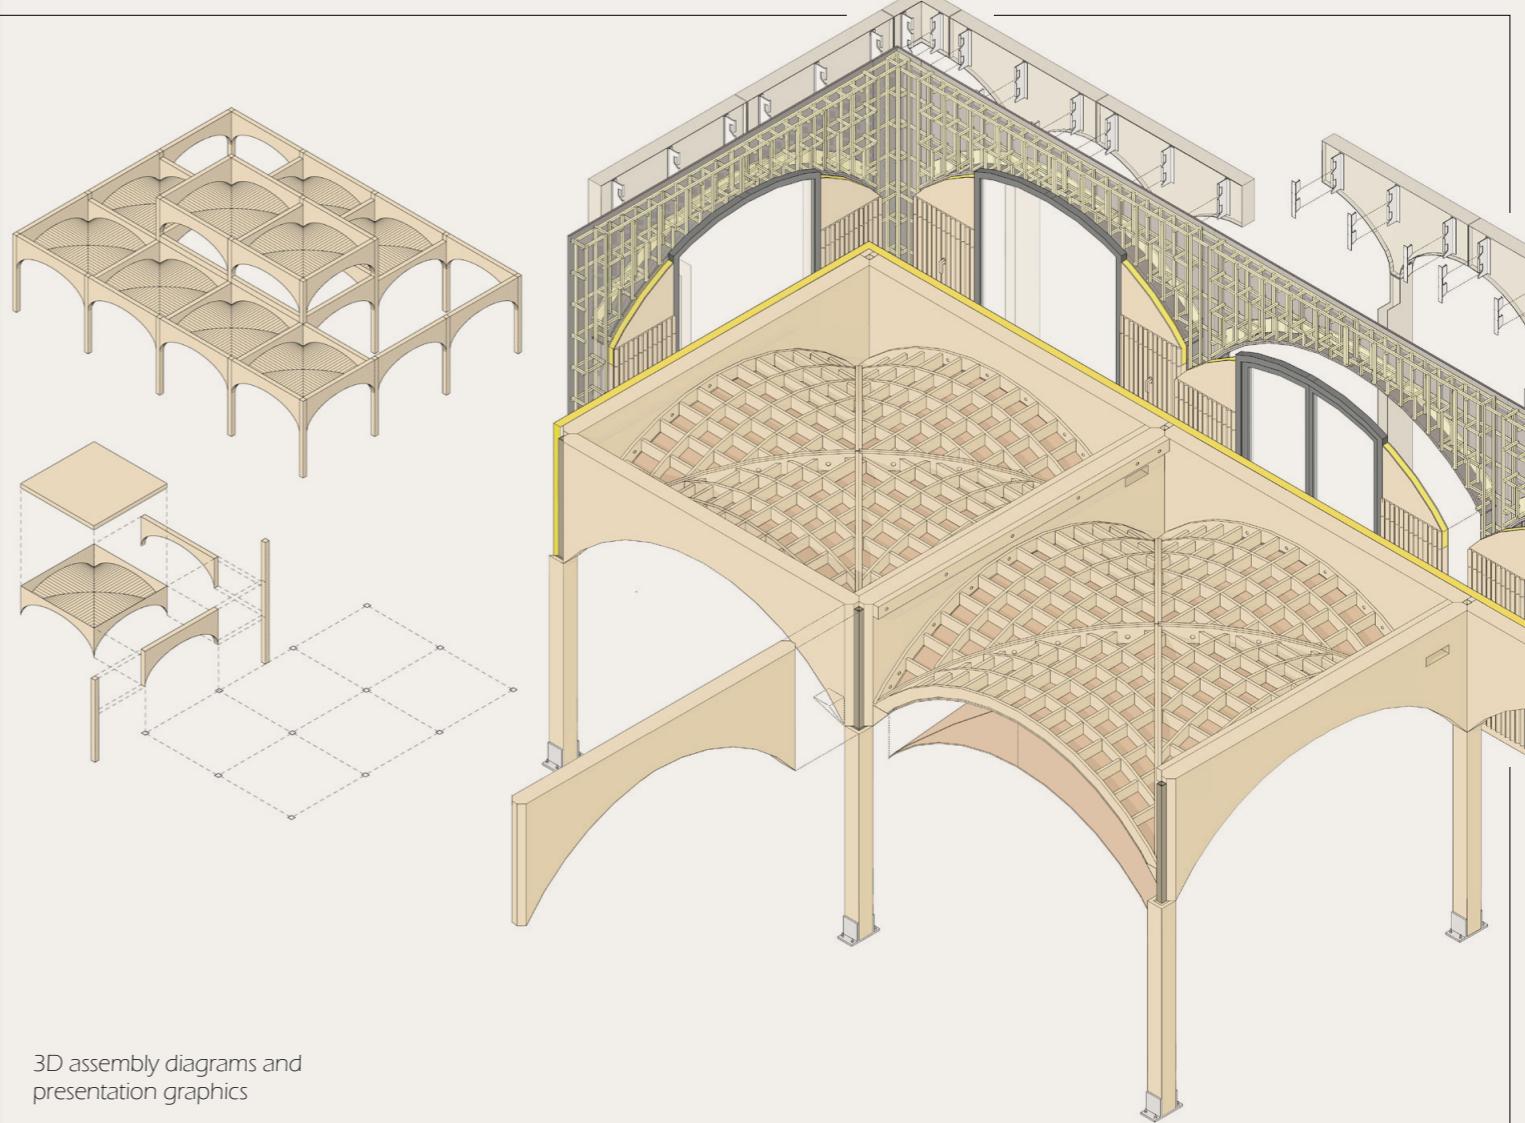


3D assembly diagrams and presentation graphics



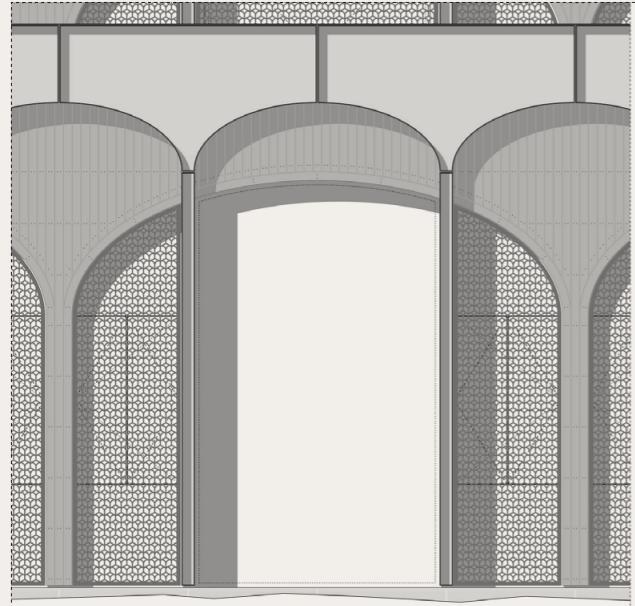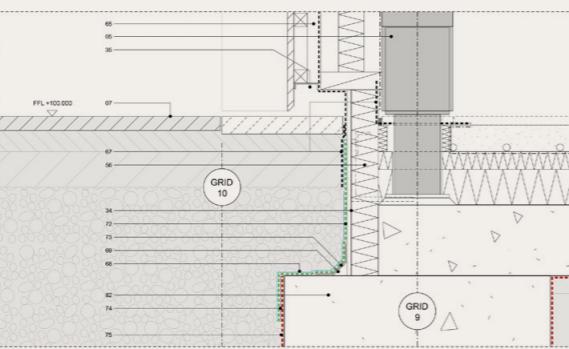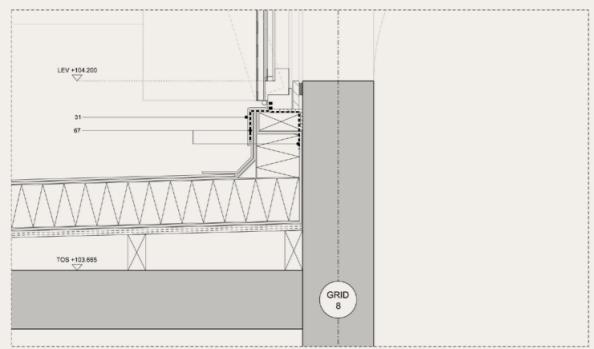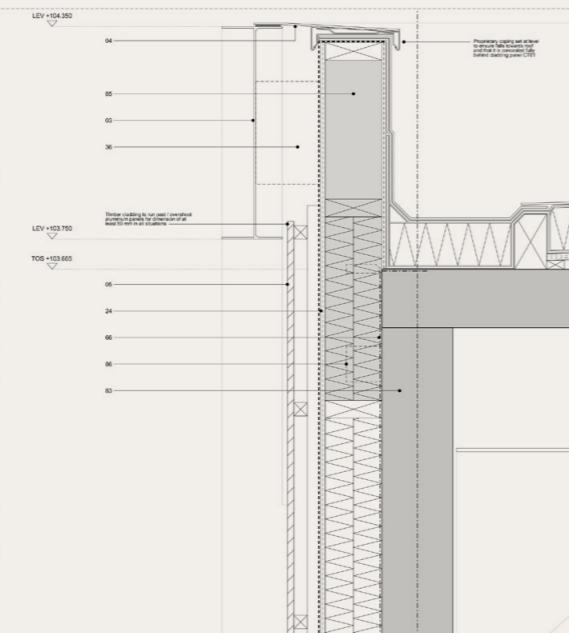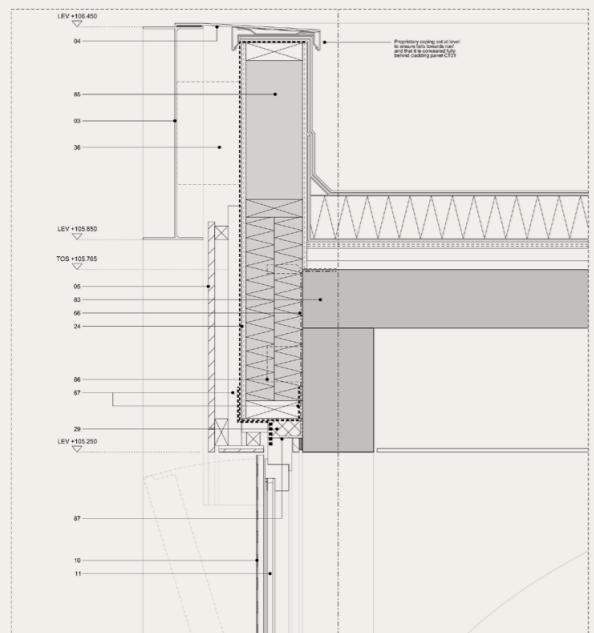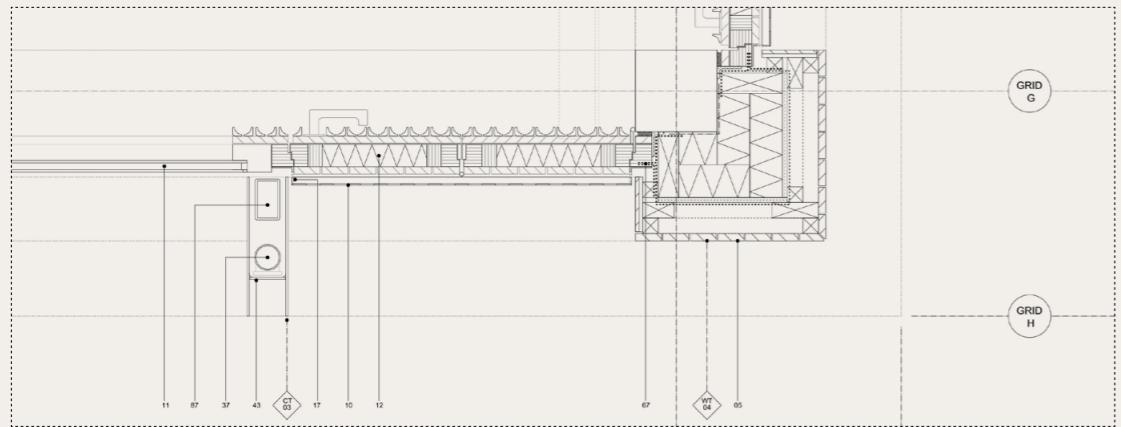

Construction drawings

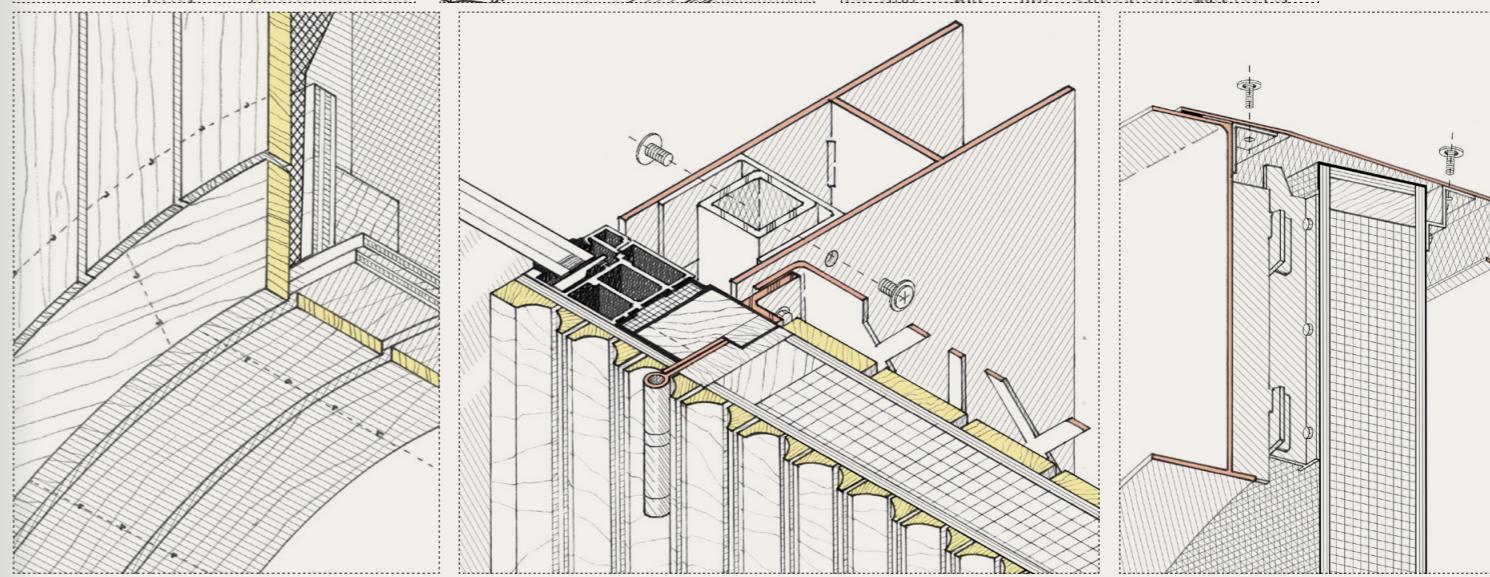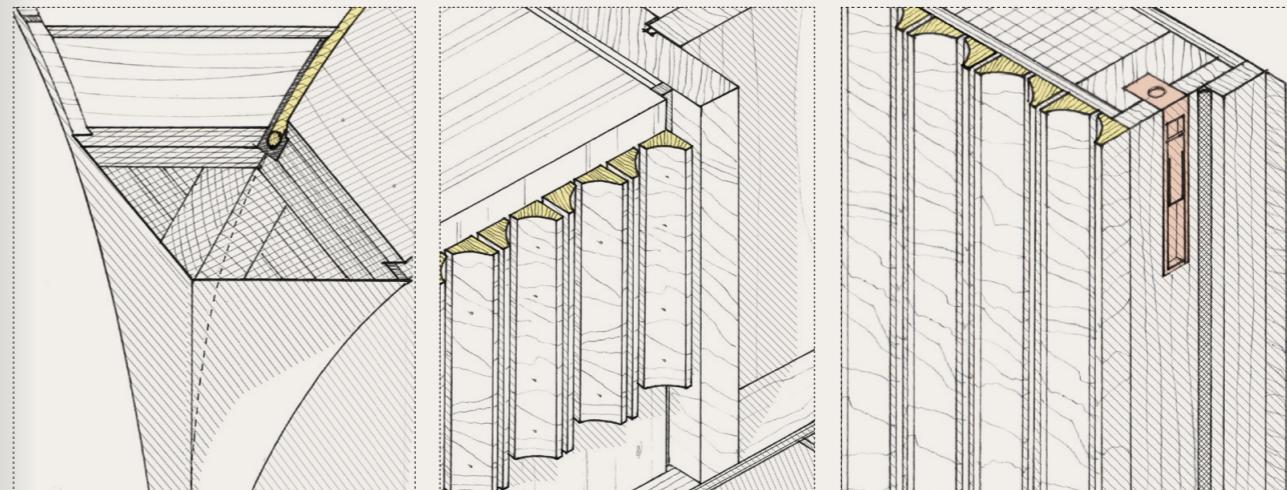

3D construction details





WILDERNESSE MEWS

For Morris + Company

**Delivery Architect
Stages 4 & 5**

Key Tasks:

Producing GA drawings & construction details


Site inspections

Coordinating contractor information

Quality control

Product specification

NBS Specification

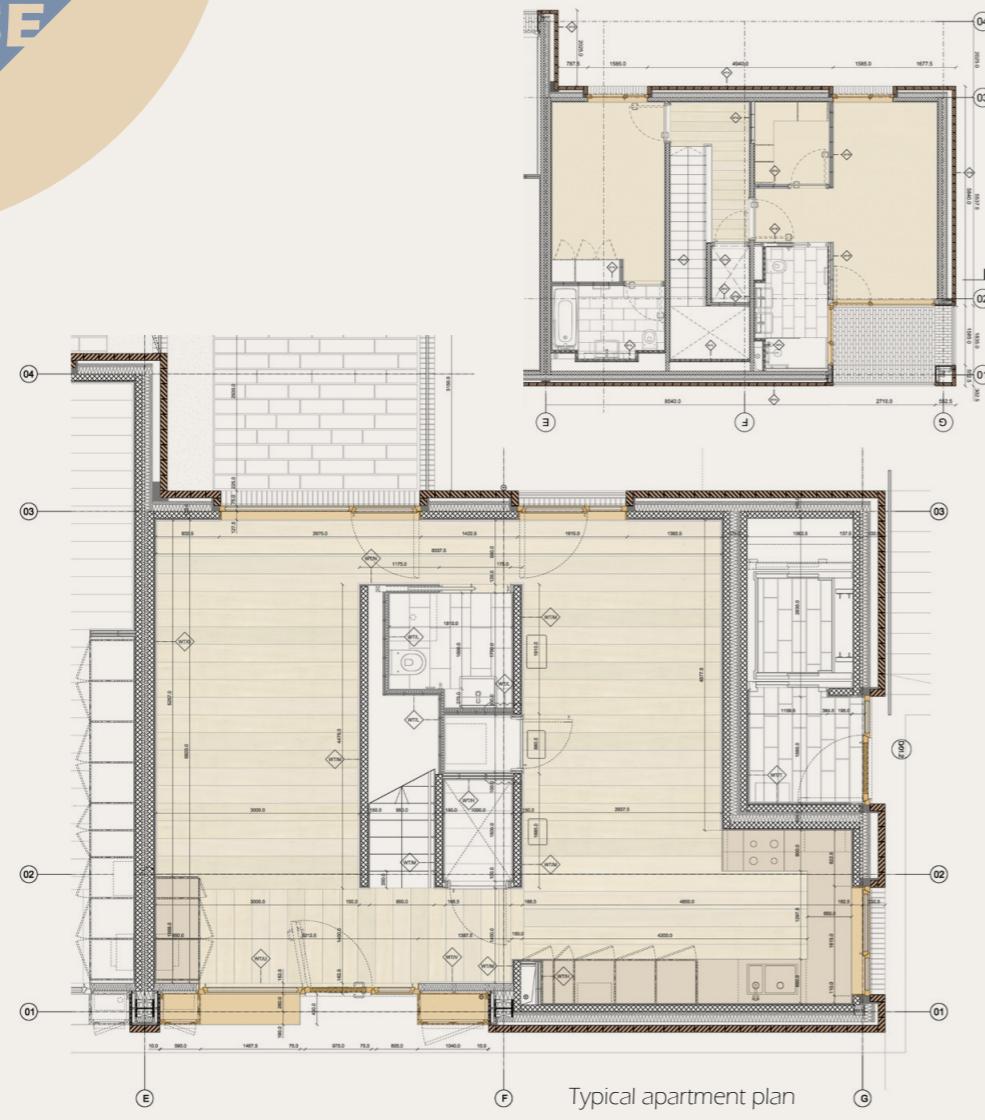


Typical apartment plan



GA elevations and GF plan



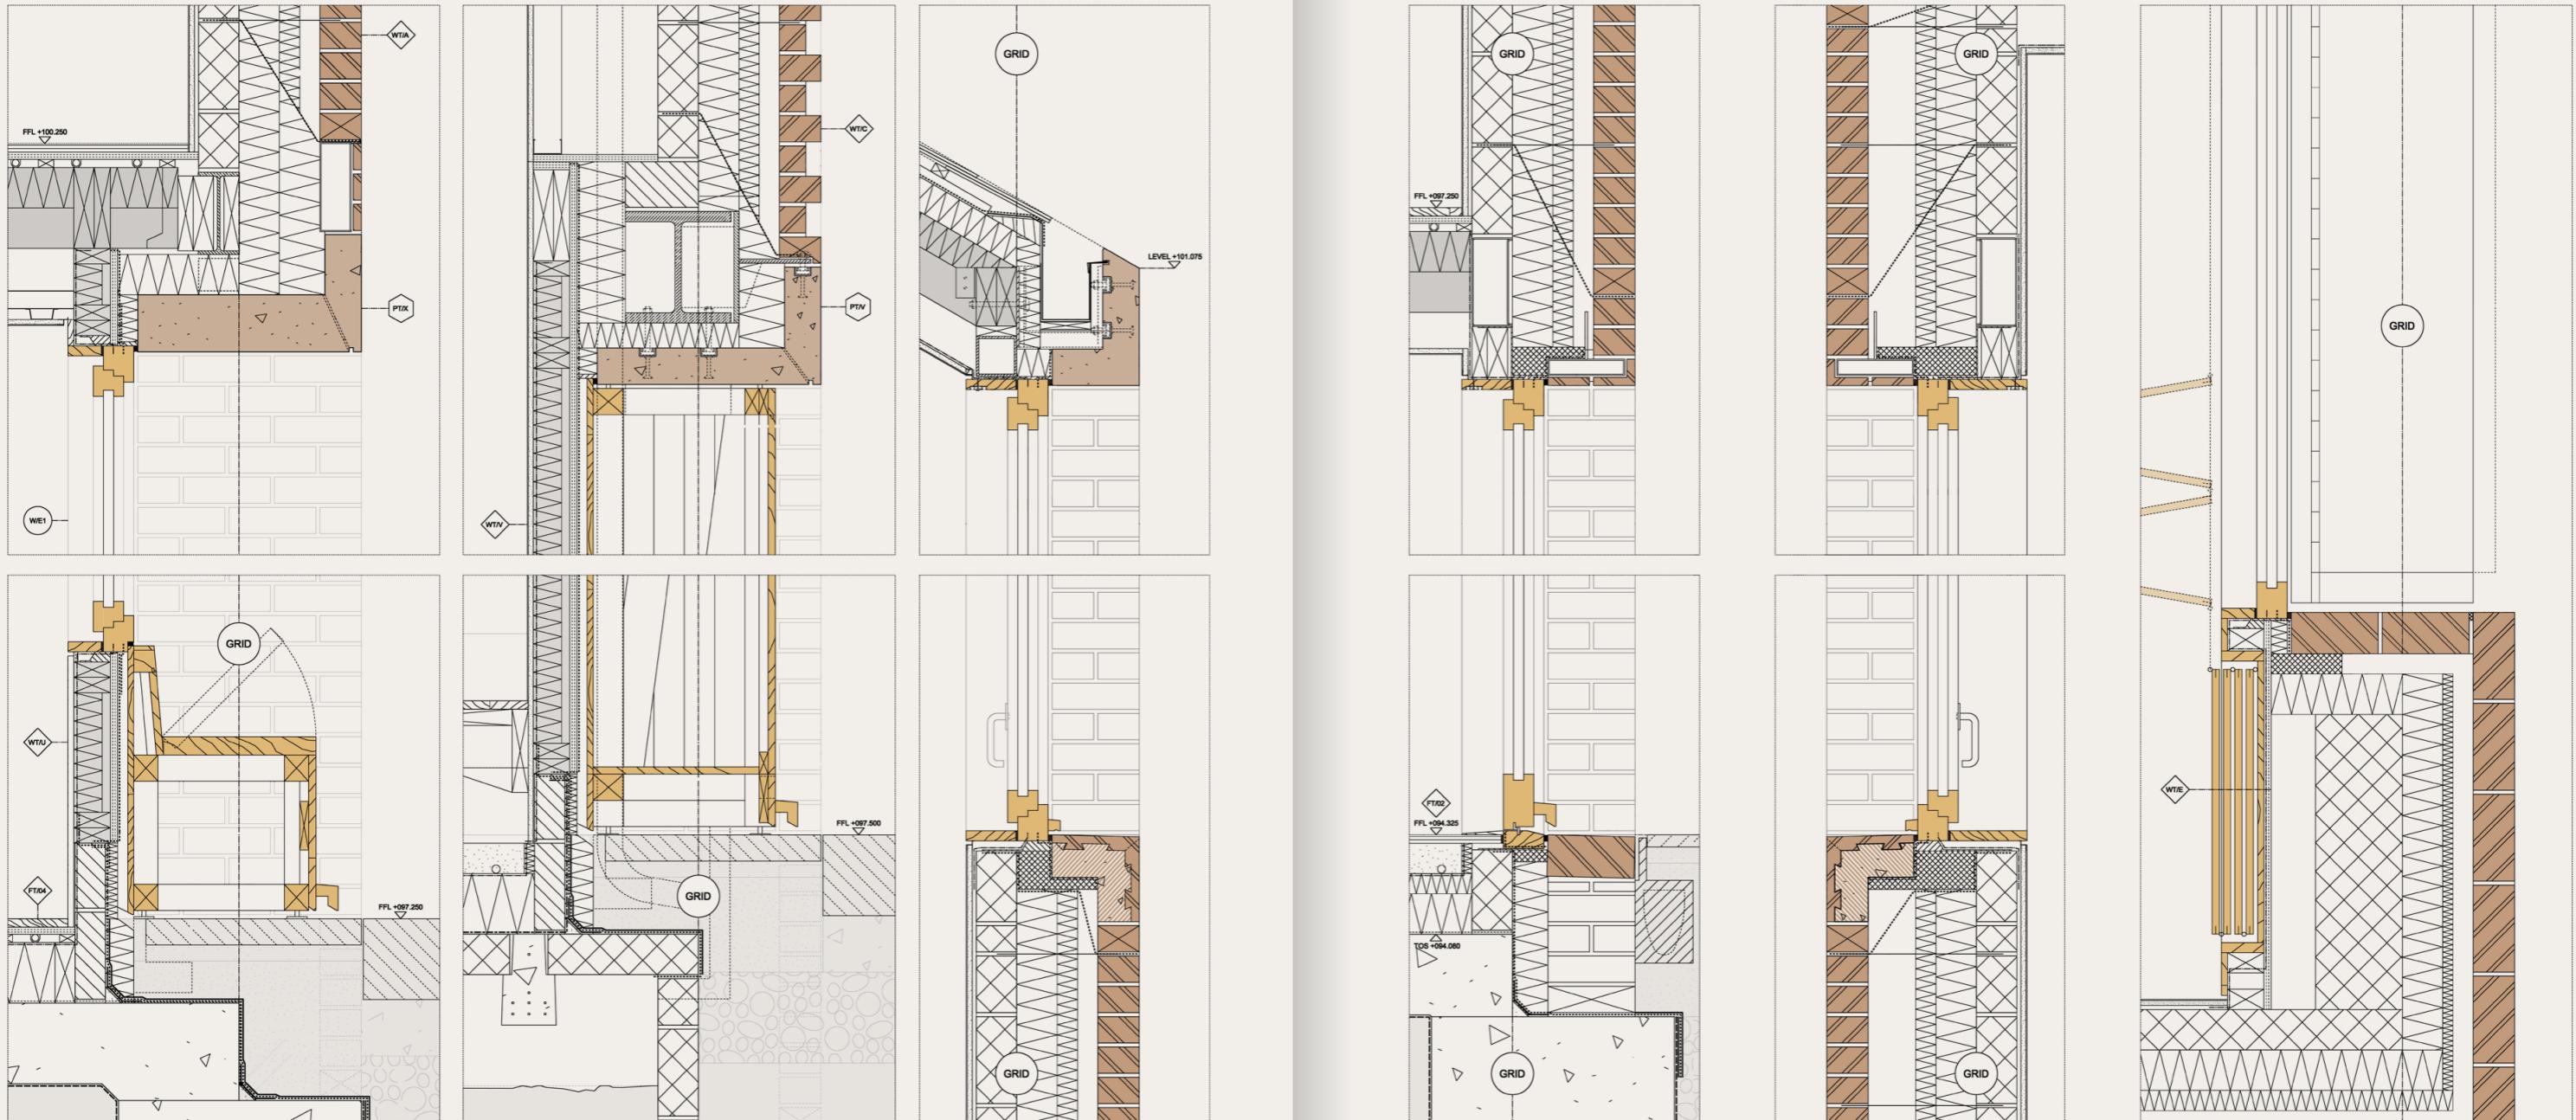

Construction details





ROCHESTER ROW For BGY

**Project Architect
Stages 1 to 4**

Key Tasks:

Production of planning information and DAS

Production for pre-apps and public consultations

Coordinating consultant information

Concept and design development

Coordination with statutory authorities

Client liaison

Rendering and 3D visuals




Conceptual 3D sketch




Detailed elevation studies



Planning elevations

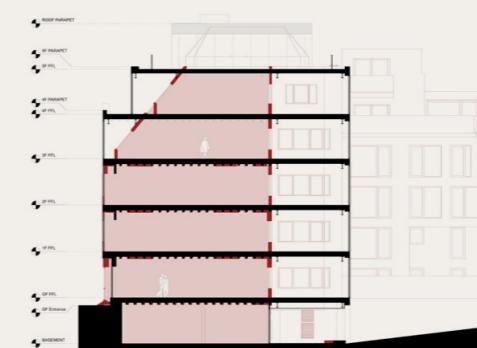

Planning GA plan and section

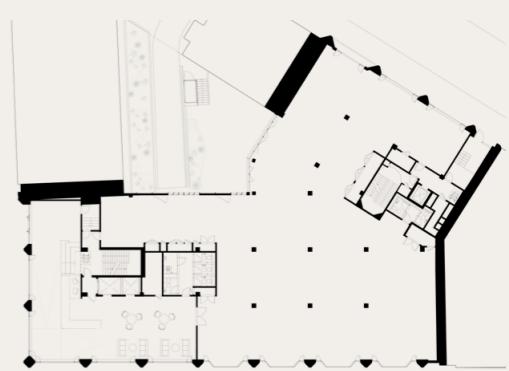



SYLVAN HERIAGE

For Morris + Company

**Project Architect
Stages 1 to 3**

Key Tasks:

Production of planning drawings and DAS



Production for pre-apps and public consultations

Coordinating consultant information


Production of visuals

Concept and design development

Coordination with statutory authorities

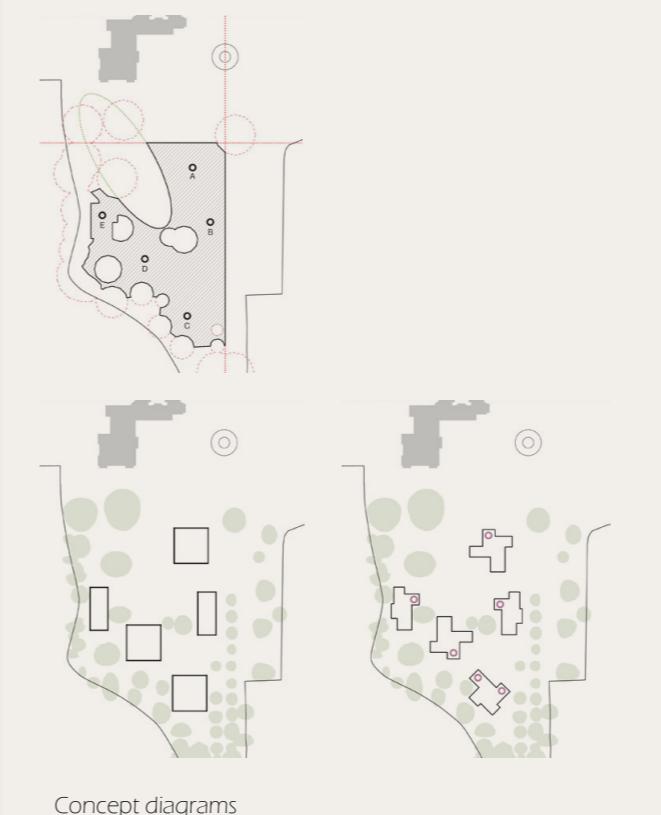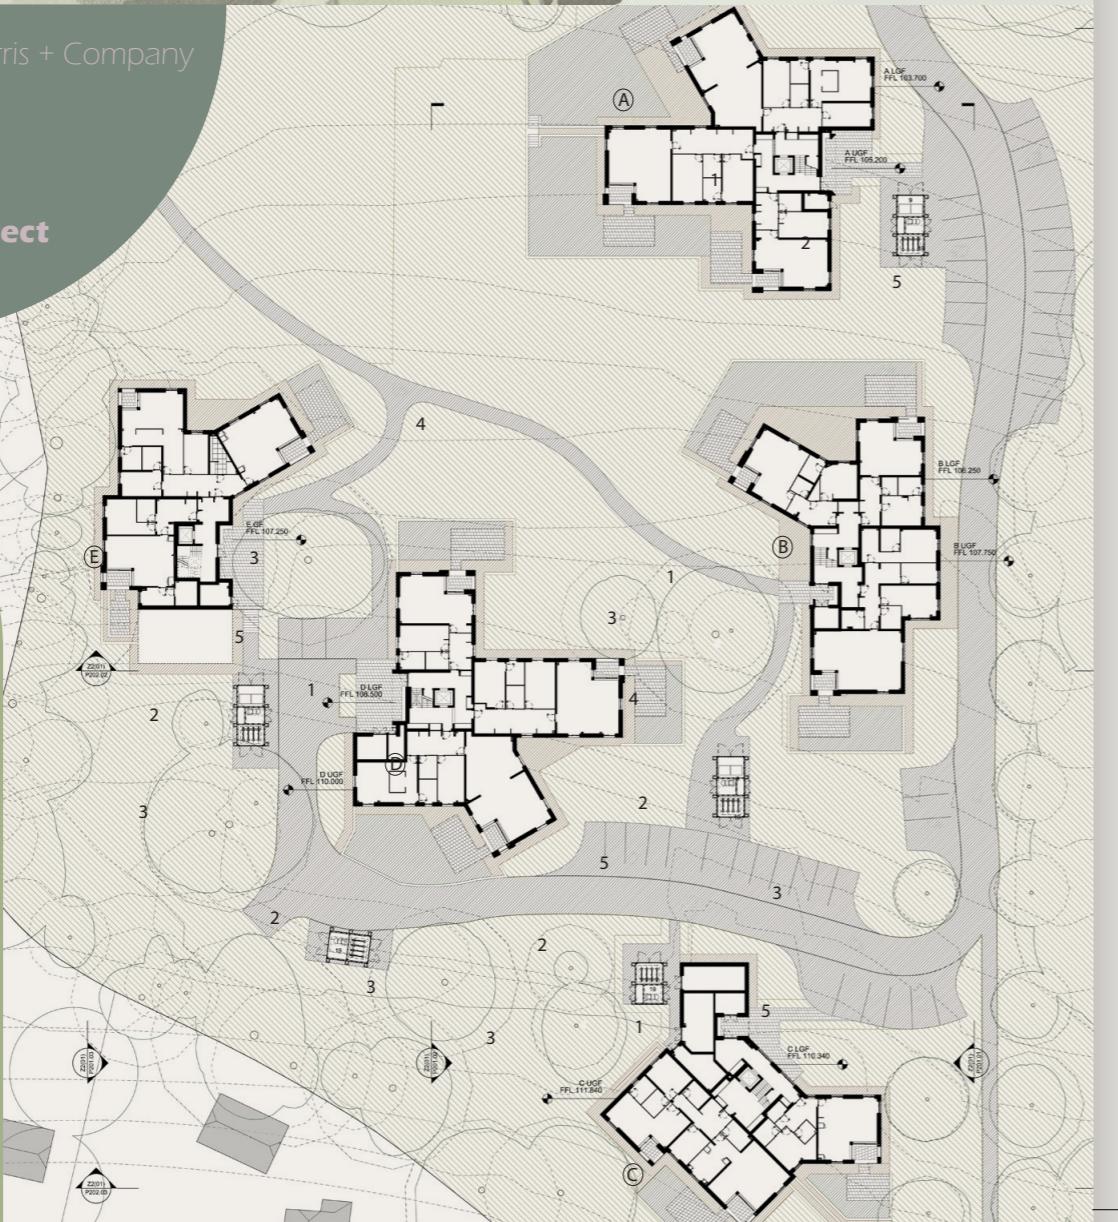

Concept diagrams

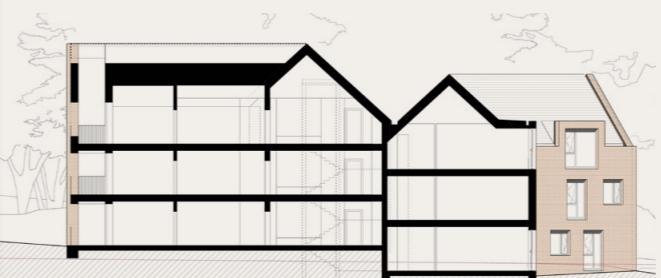

GA Elevations and Sections



Rendered elevations






THE PLINTH

For Mowbray Crawshaw Architects

**Delivery Architect
Stages 4 & 5**

Key Tasks:

- Production of planning drawings and DAS
- Production for pre-apps and public consultations
- Coordinating consultant information
- Production of visuals
- Concept and design development and incorporation of client brief

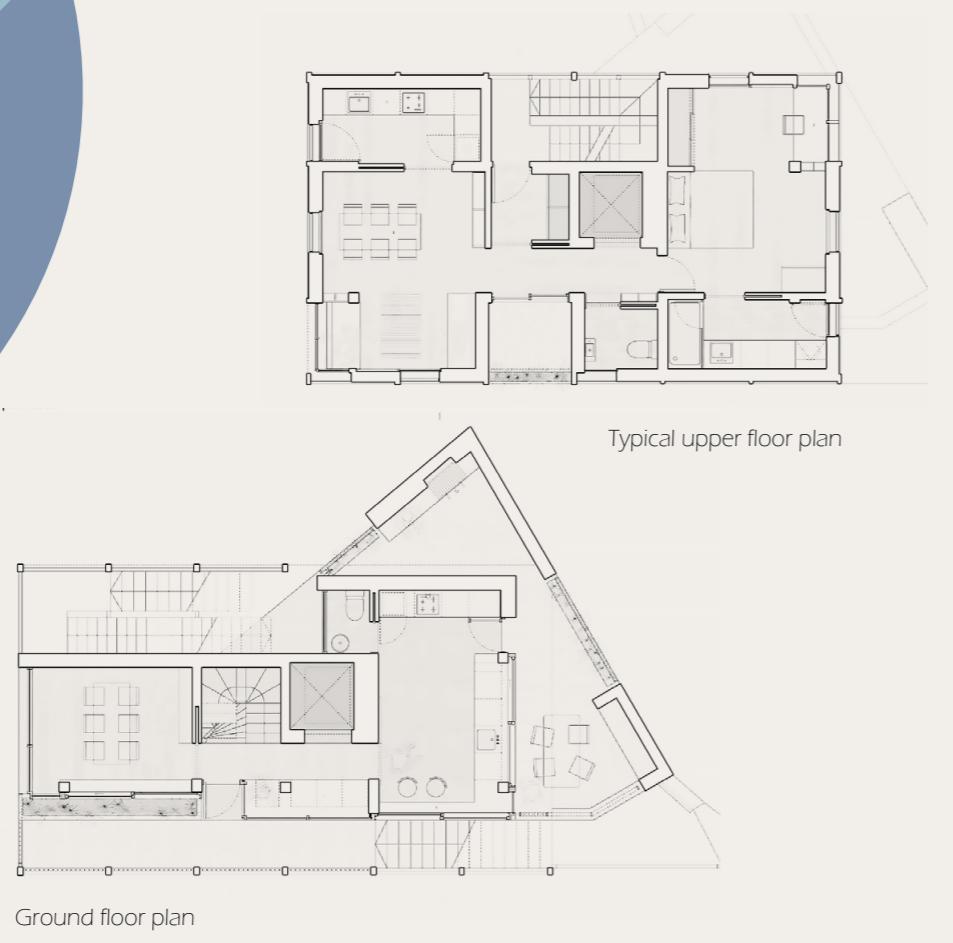



CRESCENT CENTRE

For BGY

**Lead Architect
Stages 3 to 5**

Key Tasks:


Detailed design of all external and internal building fabric for construction

Coordination with consultants


Coordination with suppliers

NBS specification

Product specification

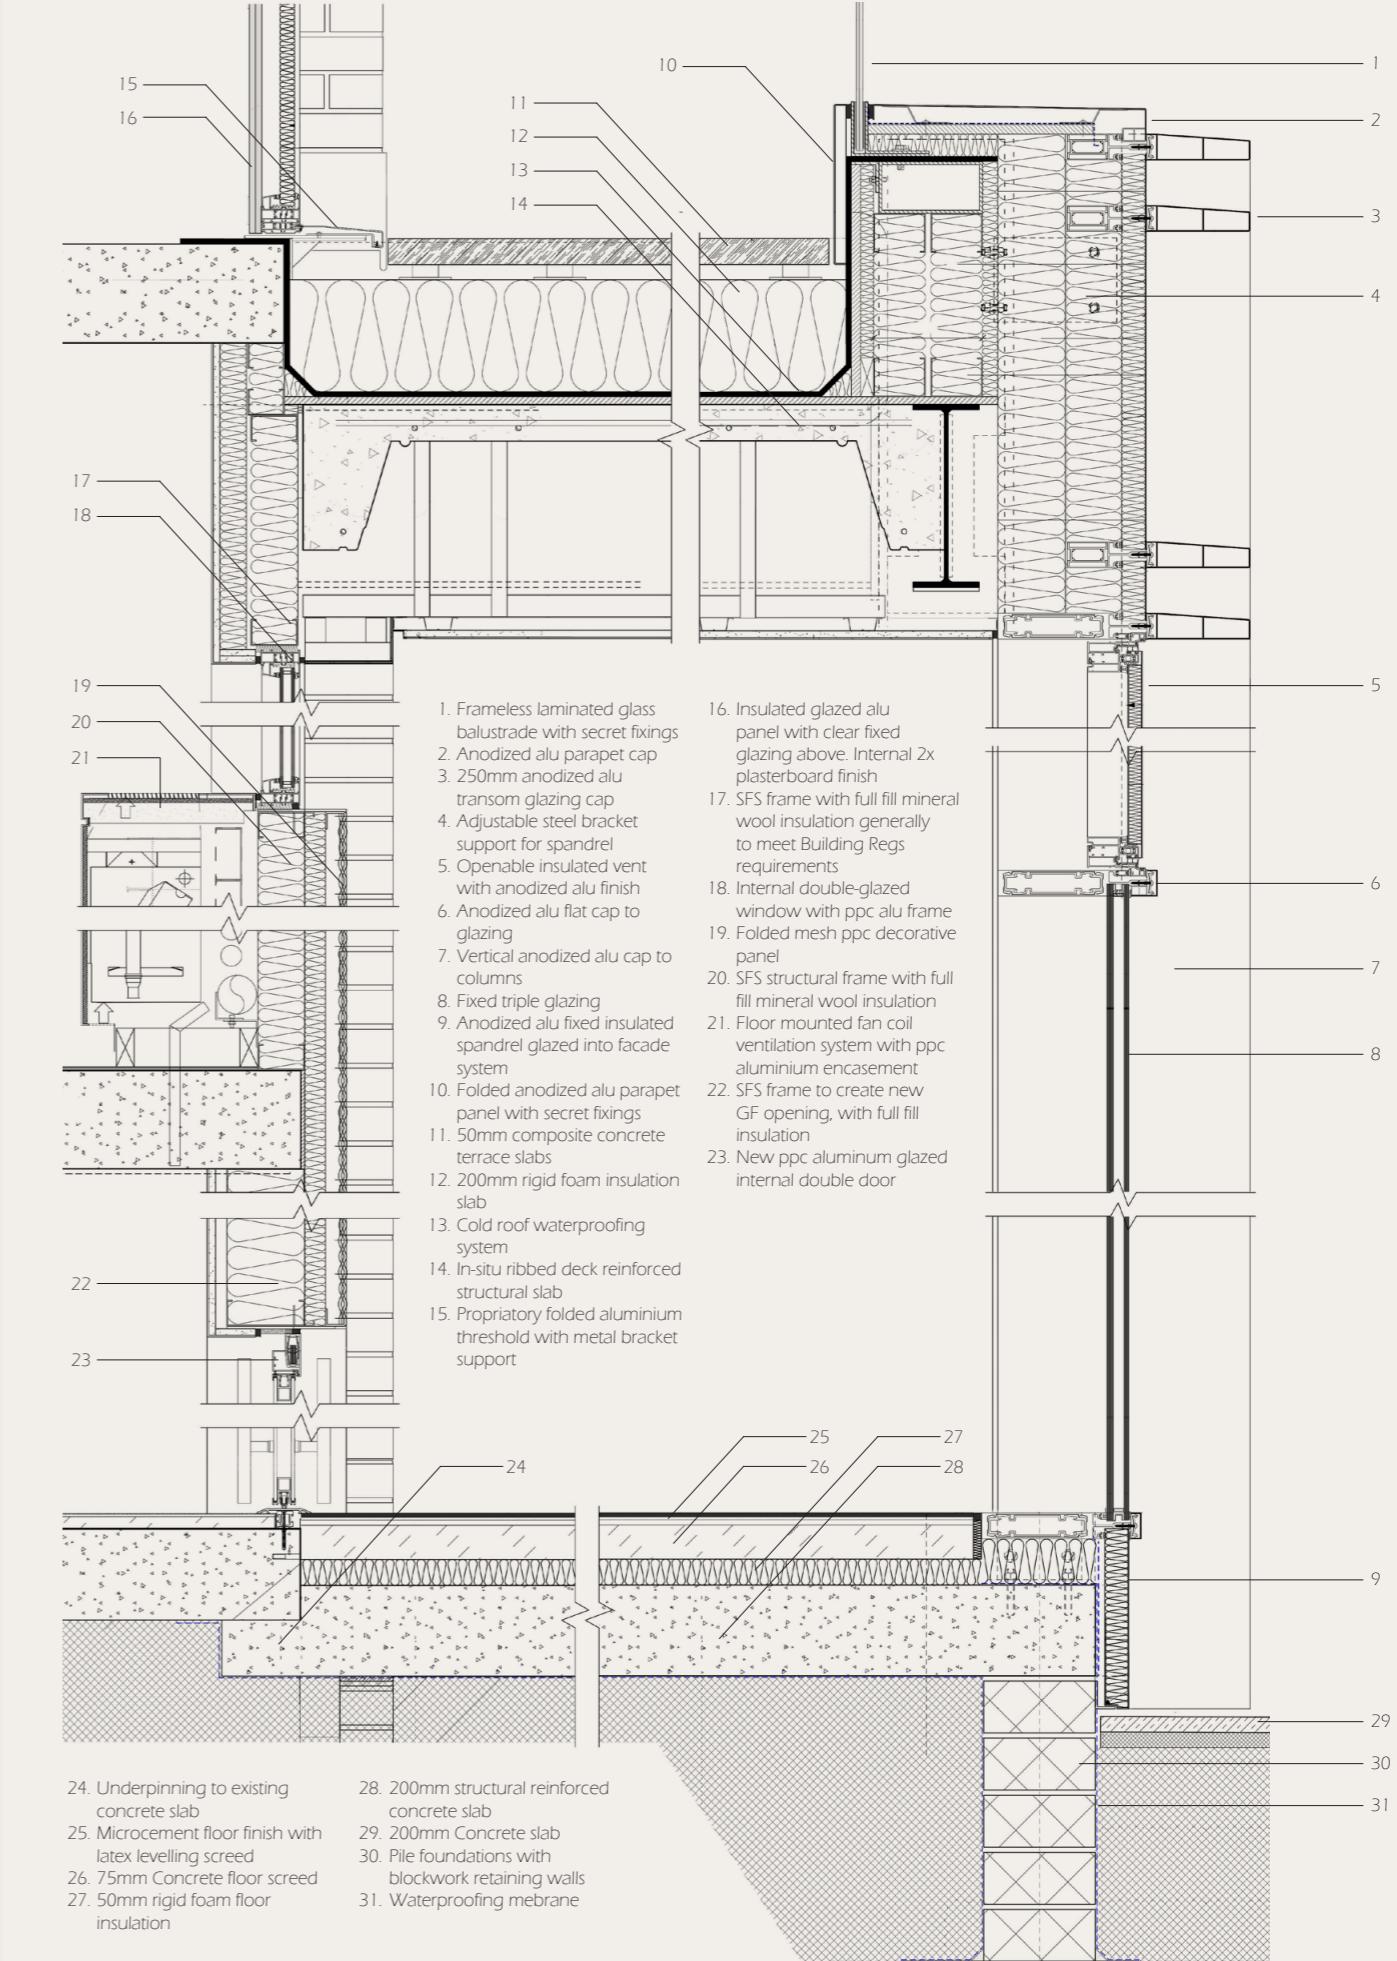

New GF extension section detail

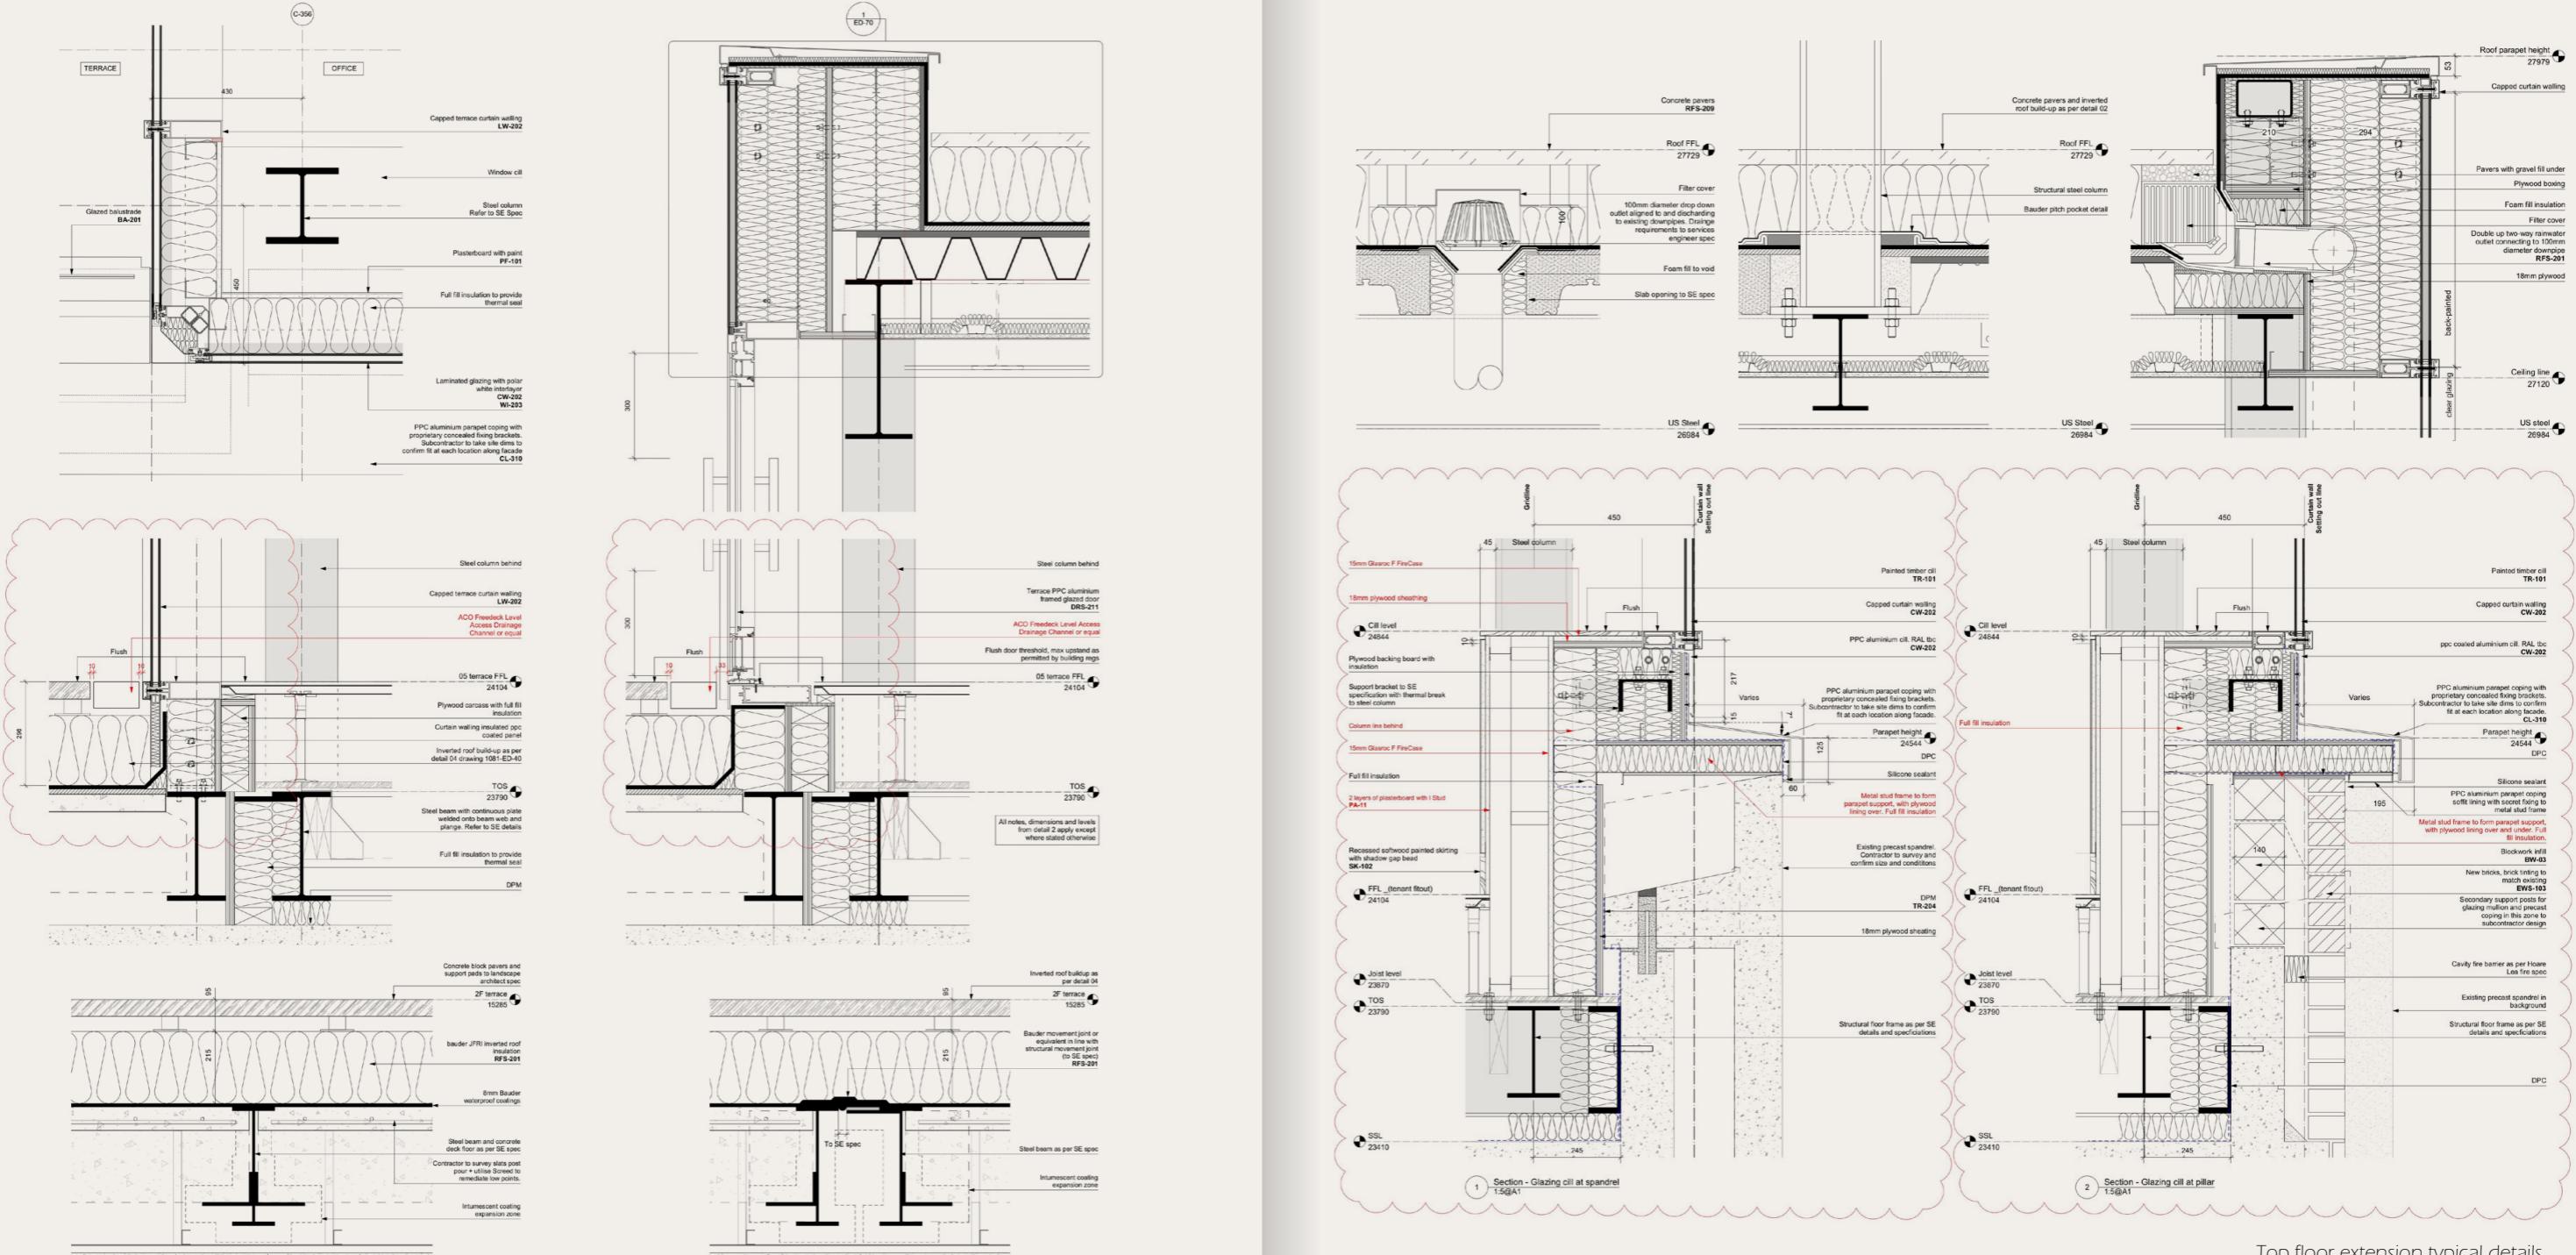

Top floor extension typical details

